


KANDOR SCHOOL, New York City, NY

Srping 2017 GSD | Instructor: Preston Scott Cohen | Kandor Architecture

Inspired by artist Mike Kelley's Kandor, this studio explores **novel forms and their spatial uses** in the case of a **K-12 school project** in Brooklyn, NYC. The disadvantage of the site is it being **sliced into two parts by a highway** entering into New York City. As a result, the formal gesture for this project is to place two blocks of classrooms on either side

of the highway, and to re-unite the site by having **two bridges of novel forms crossing the highway both above and under it**. The two blocks flanking the highway are the conventional classrooms; the two bridges are filled with programs that foster interaction, such as libraries, dining halls and multi-function rooms.

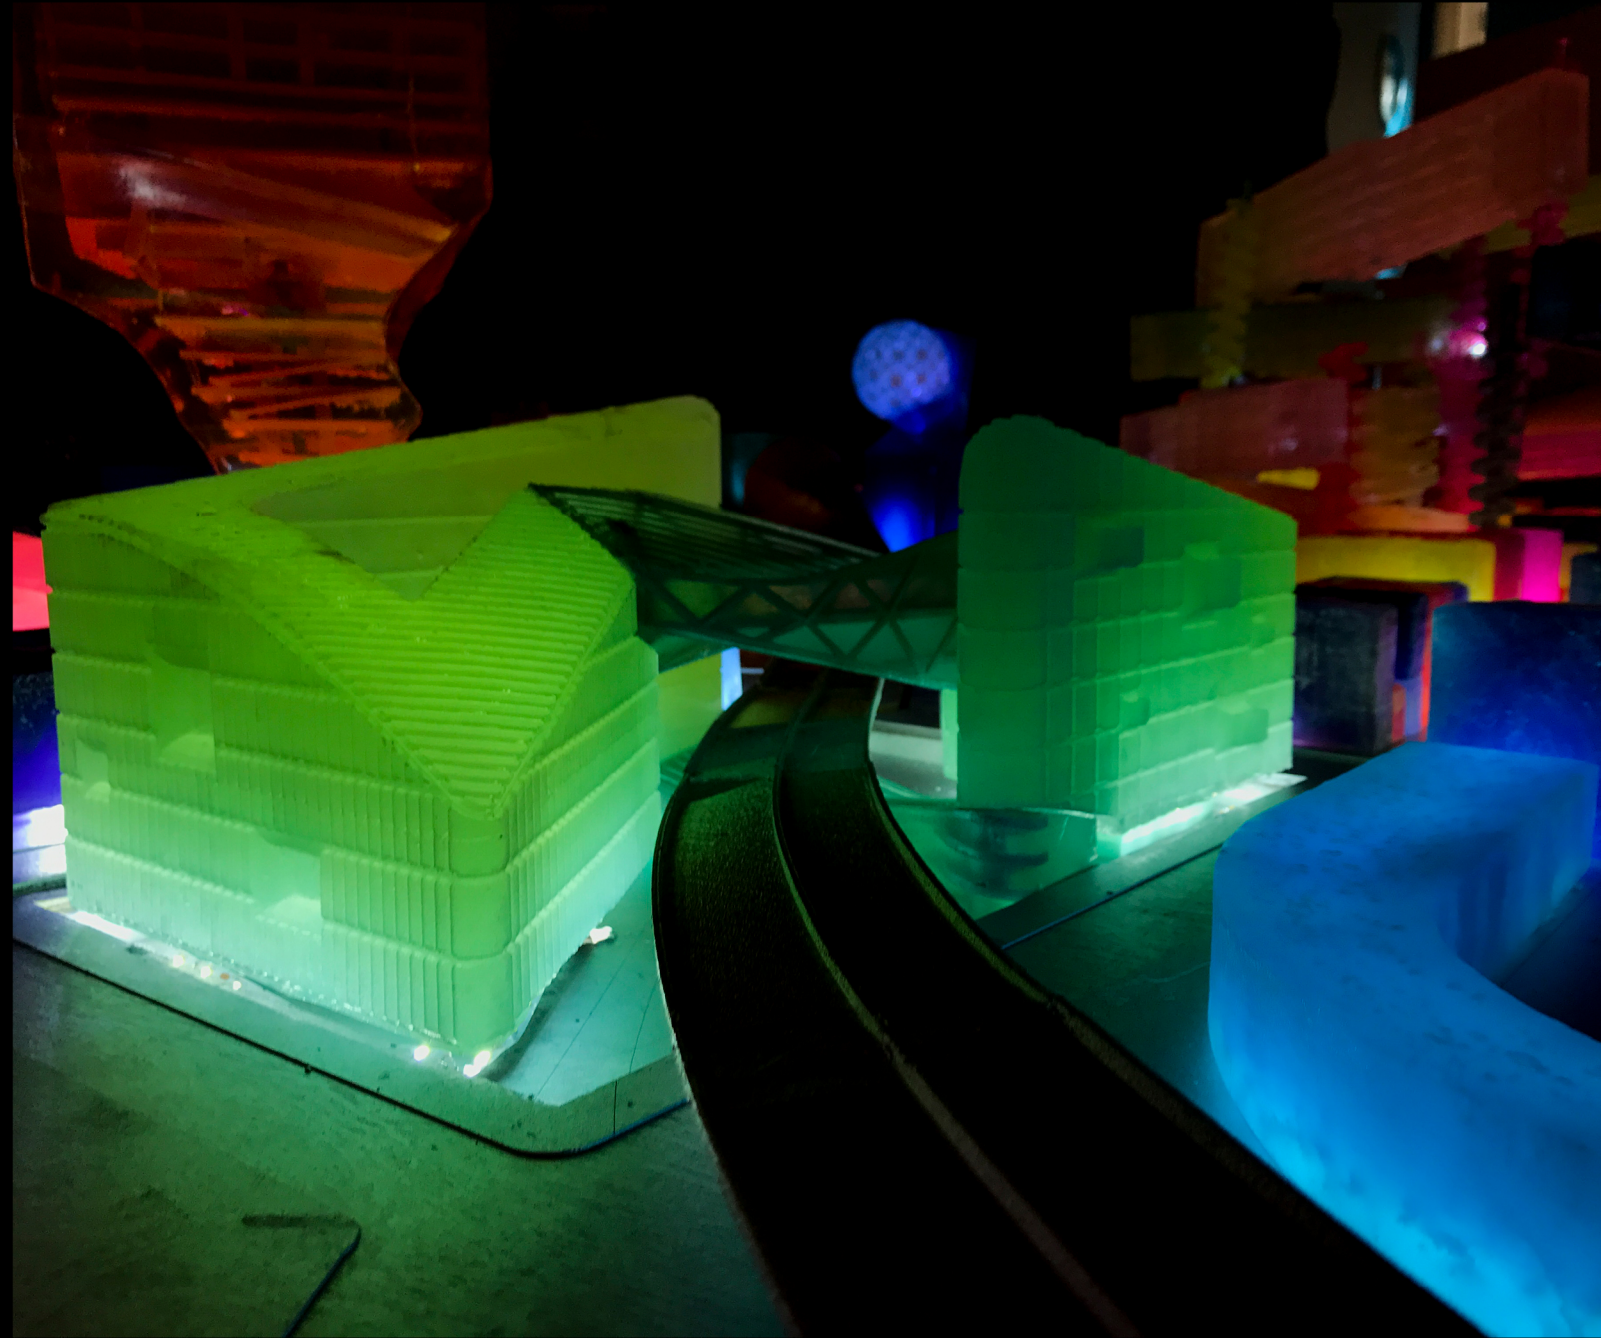





Kandor by Artist Mike Kelley




Final Model in Context

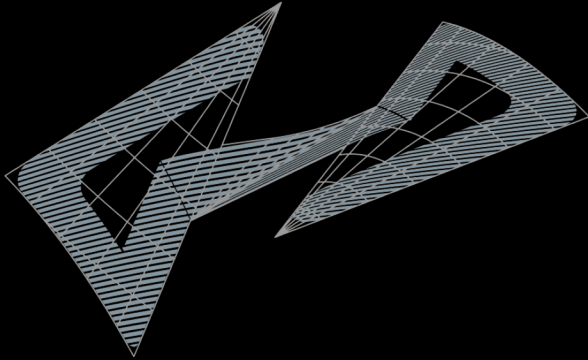

Geometry Diagram

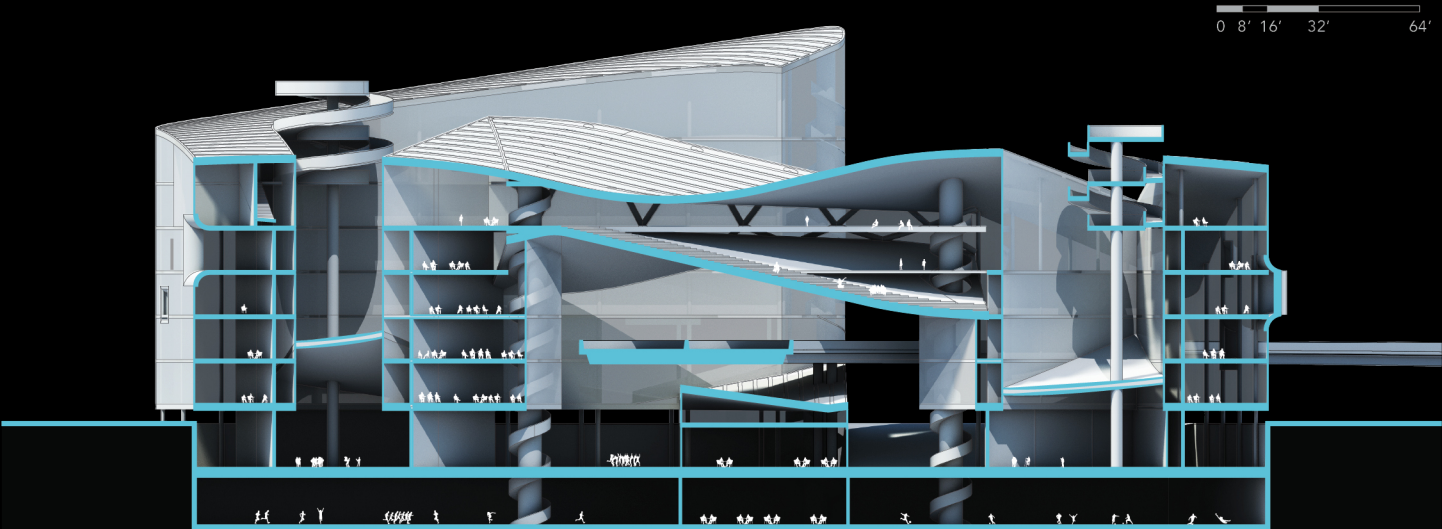

Longitudinal Section

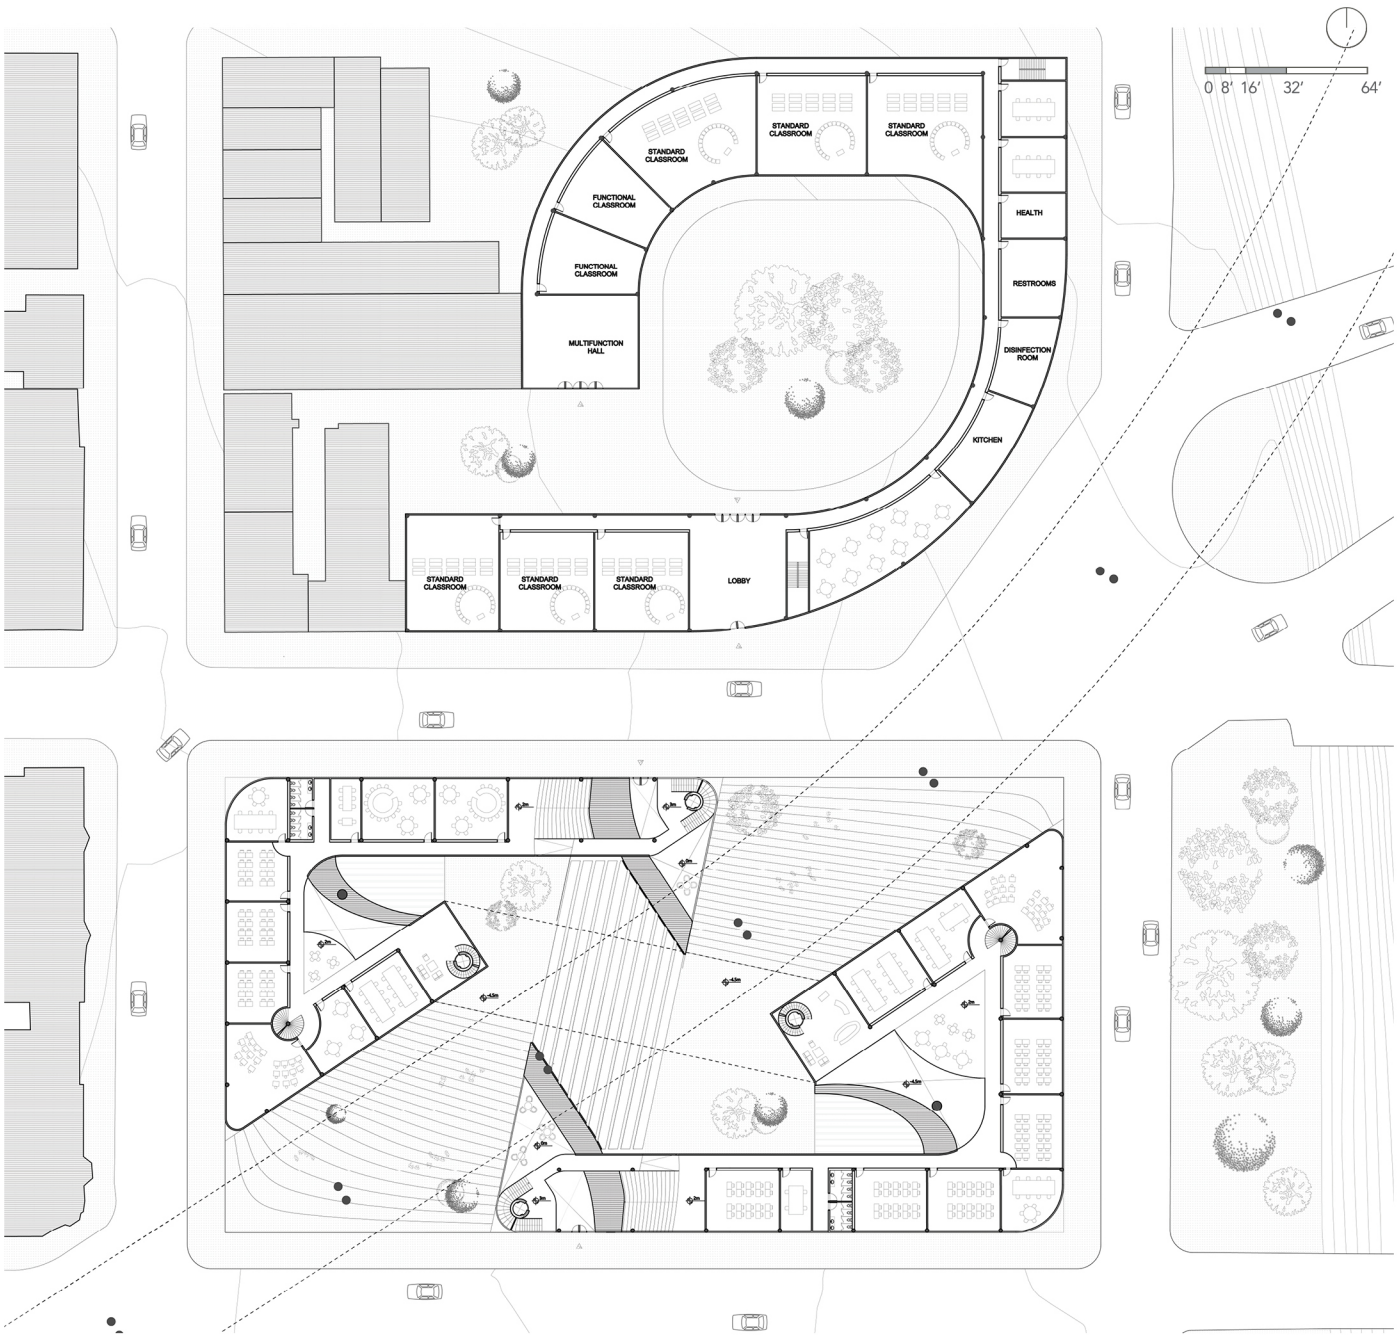

Ground Floor Plan

